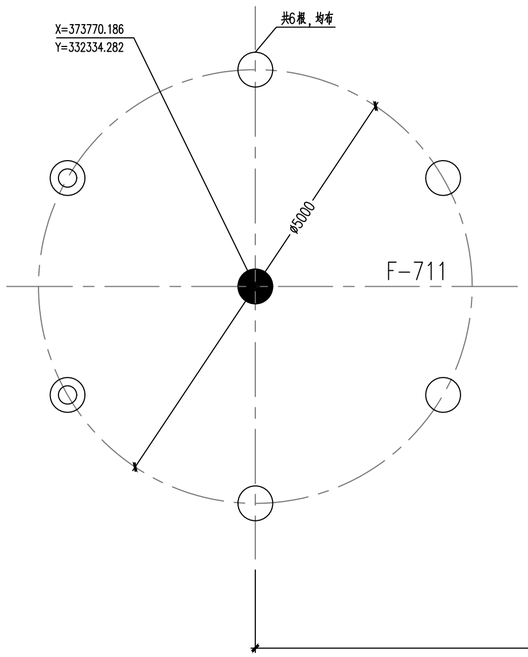

乙二醇罐区桩位图 1:50

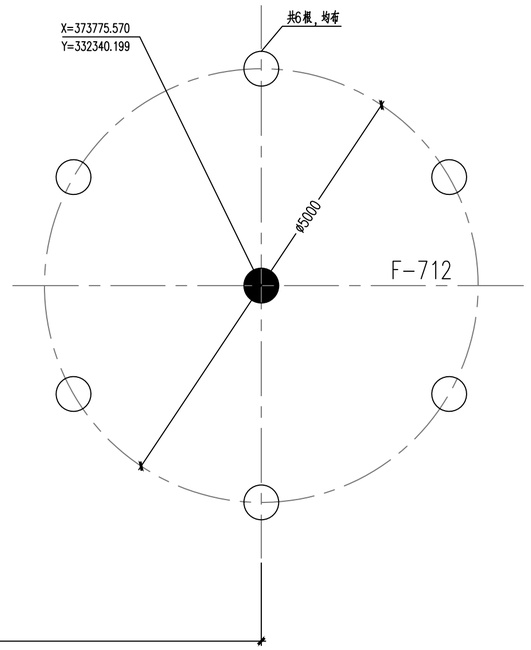

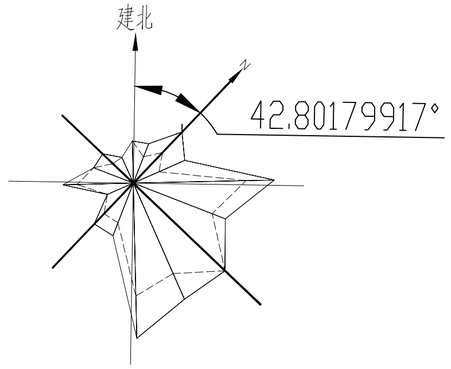

基桩施工说明：

1、图中标高以米计，尺寸以毫米计，标高±0.000相当于绝对标高7.200。
2、地基基础设计等级：乙级。建筑桩基设计等级：乙级。
3、桩端持力层为③-2层粉质黏土层，桩身必须全截面进入此层不小于1000mm。
4、②-1层为液化土层，桩身配筋需加强设置：
上两节桩中②号螺旋箍筋全长范围内加密设置，下节桩中加密区长度同图集。
5、成桩后，桩基检测前的休止时间不应少于25天。
6、桩基检测：
1）单桩竖向承载力检测：采用高应变。
2）桩身完整性检测：采用低应变检测。
7、施工前应先试桩，试桩数量不应少于2根。试桩最大静压力为1100kN。
8、桩基检测按照按《建筑地基基础检测规程》(DB 32/39 16-2020)有关规定执行。
9、其他未尽事宜详见【地基基础及桩基工程说明】。

桩参数一览表

桩图例	名称	型号	预估单桩竖向承载力特征值 Ra（考虑液化及负摩阻）(kN)	单桩水平承载力特征值 Rha (kN)	桩端持力层	桩顶相对标高(m)	桩长(m)	数量(根)	备注
●	工程桩兼试桩	(PHC400AB95-12)+(PHC400AB95-8)+(PHC400AB95-7)+b	550kN(500kN)	35kN	③-2	-0.700	27	2	非抗拔桩
○	工程桩	(PHC400AB95-12)+(PHC400AB95-8)+(PHC400AB95-7)+b	550kN(500kN)	35kN	③-2	-0.700	27	10	非抗拔桩
◎	工程桩	(PHC400AB95-12)+(PHC400AB95-7)+(PHC400AB95-7)+b	550kN(500kN)	35kN	③-2	-0.700	26	2	非抗拔桩

版次	说明	设计	校对	审核	审定	专业负责人	项目负责人	日期
1								
0	供施工	李文娜	李文	戴永红		戴永红	吕成成	20260315

华东工程 Huadong Engineering

安徽华东化工医药工程有限责任公司
ANHUI HUADONG CHEMICAL AND MEDICAL ENGINEERING CO., LTD

The copyright of this drawing is the property of ANHUI HUADONG CHEMICAL AND MEDICAL ENGINEERING CO., LTD.
Unauthorized disclosure or duplication to the third party is not permitted.

业主 CLIENTS	江苏德纳化学股份有限公司			图名 DRAWING NAME	乙二醇罐区桩位图
项目 PROJECT	6万吨/年环氧乙烷装置产品提升及附属设施项目				
装置/工区 UNIT & WORK AREA	乙二醇罐区（扩建）			项目号 PROJECT NO.	N25001
设计阶段 DESIGN STAGE	施工图	专业 SPEC.	结构	比例 SCALE	图示	图号 DRAWING NO.	N25001D104CV01DW02

给排水 | 电气 | 暖通 | 专业 | 签字 | 日期
总图 | 建筑 | 结构 | 专业 | 签字 | 日期
工艺 | 设备 | 自控 | 专业 | 签字 | 日期