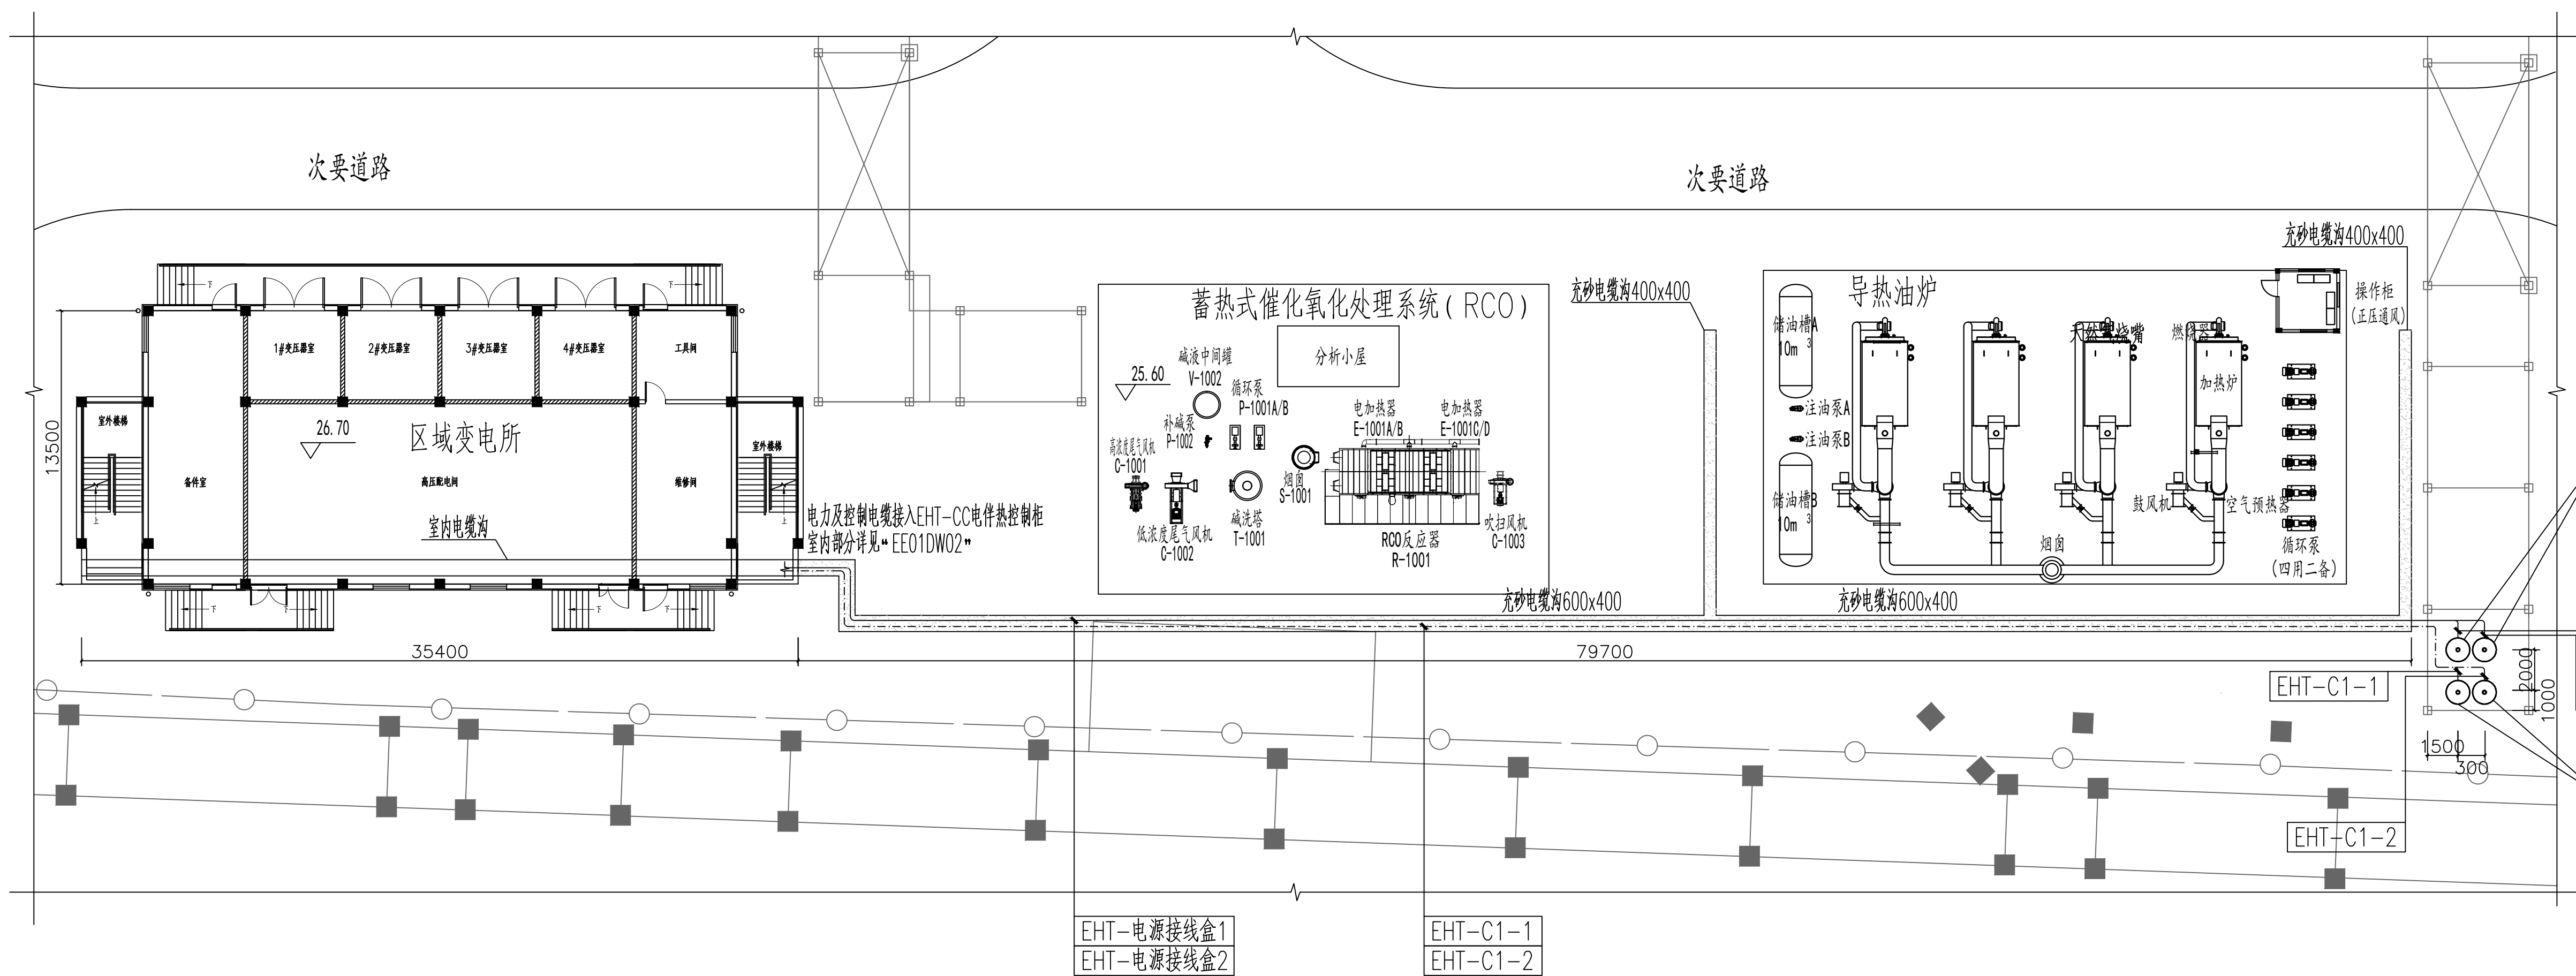


图 例

| 符号 | 说 明   |
|----|-------|
|    | 防爆接线盒 |
|    | 电力电缆  |
|    | 控制电缆  |
|    | 充砂电缆沟 |

说明:

- 由EHT-CC电伴热控制柜至防爆电源接线盒及防爆测温接线盒电缆的室外部分沿现有充沙电缆沟敷设。电缆出电缆沟后埋地敷设，埋地深度0.7m，沿钢柱引上，出地面处穿金属管保护。
- 本次新增EHT电源防爆接线盒及防爆测温接线盒各2只。接线盒位于导热油炉工区东南侧系统管架旁，乙烯焦油管道中心标高为距地3.2m，电伴热接线盒位于管道上方0.3米。测温接线盒和电源接线盒间距约2m，具体位置可根据现场实际情况做相应调整，图中仅为示意。电缆长度需根据现场实测后下料。
- 电缆及保护管开料详见“D01EE01DW08 电缆作业表”
- EHT电源防爆接线盒及防爆测温接线盒由厂家配套提供，本设计不开料。接线盒位于爆炸危险场所，防爆等级不低于dIIBT4或eIIBT4。
- 平面图中尺寸单位为mm。

|   |                       |              |             |                   |        |             |
|---|-----------------------|--------------|-------------|-------------------|--------|-------------|
|   |                       | 冯耀文          | 吴建红         | 吴卓平               |        |             |
|   |                       | 同耀文          | 吴建红         | 吴卓平               |        | 2026.03.15  |
| 版次   | 说 明                   | 设计           | 校核          | 审核                | 批准     | 日期          |
| REV   | DESCRIPTION           | PRE'D        | CHKD        | APPR              | AUTH'D | DATE        |
| <b>华东工程</b> 安徽华东化工医药工程有限责任公司<br>ANHUI HUADONG CHEMICAL AND MEDICAL ENGINEERING CO., LTD   |                       |              |             |                   |        |             |
| 本图纸版权为安徽华东化工医药工程有限责任公司所有, 未经本公司许可不得转让或复制给第三方。<br>The copyright of this drawing is the property of ANHUI HUADONG CHEMICAL AND MEDICAL ENGINEERING CO., LTD.<br>Unauthorized disclosure or duplication to the third party is not permitted. |                       |              |             |                   |        |             |
| 业 主   | 南京扬子精细化工有限责任公司        | 图 名          | 室外电缆走向图 (一) |                   |        |             |
| 项 目   | 至扬巴原裂解汽油管线变更为乙烯焦油管线项目 | DRAWING NAME |             |                   |        |             |
| 装置/工区   | 厂外管道部分                | 项目号          | N25024      |                   |        |             |
| 设计阶段   | 详细设计                  | 专 业          | 电 气         | 比 例               | 1:200  | 图 号         |
| DESIGN STAGE   |                       | SPEC.        |             | SCALE             |        | DRAWING NO. |
|   |                       |              |             | N25024D01EE01DW05 |        |             |