



说明：  
本图根据“南京金陵石化工程设计有限公司，南京长江江字环保科技有限公司 5万吨/年电子化学品精制再生循环利用项目 全厂电信 火灾报警系统 火灾报警系统图 22163AS060TC01DW01A0”进行绘制。

工程勘察资质(出图)专用章  
安徽华东化工医药工程有限责任公司  
化工石化医药行业甲级 证书编号:A134008172  
中华人民共和国住房和城乡建设部监制  
有效期至2029年09月20日

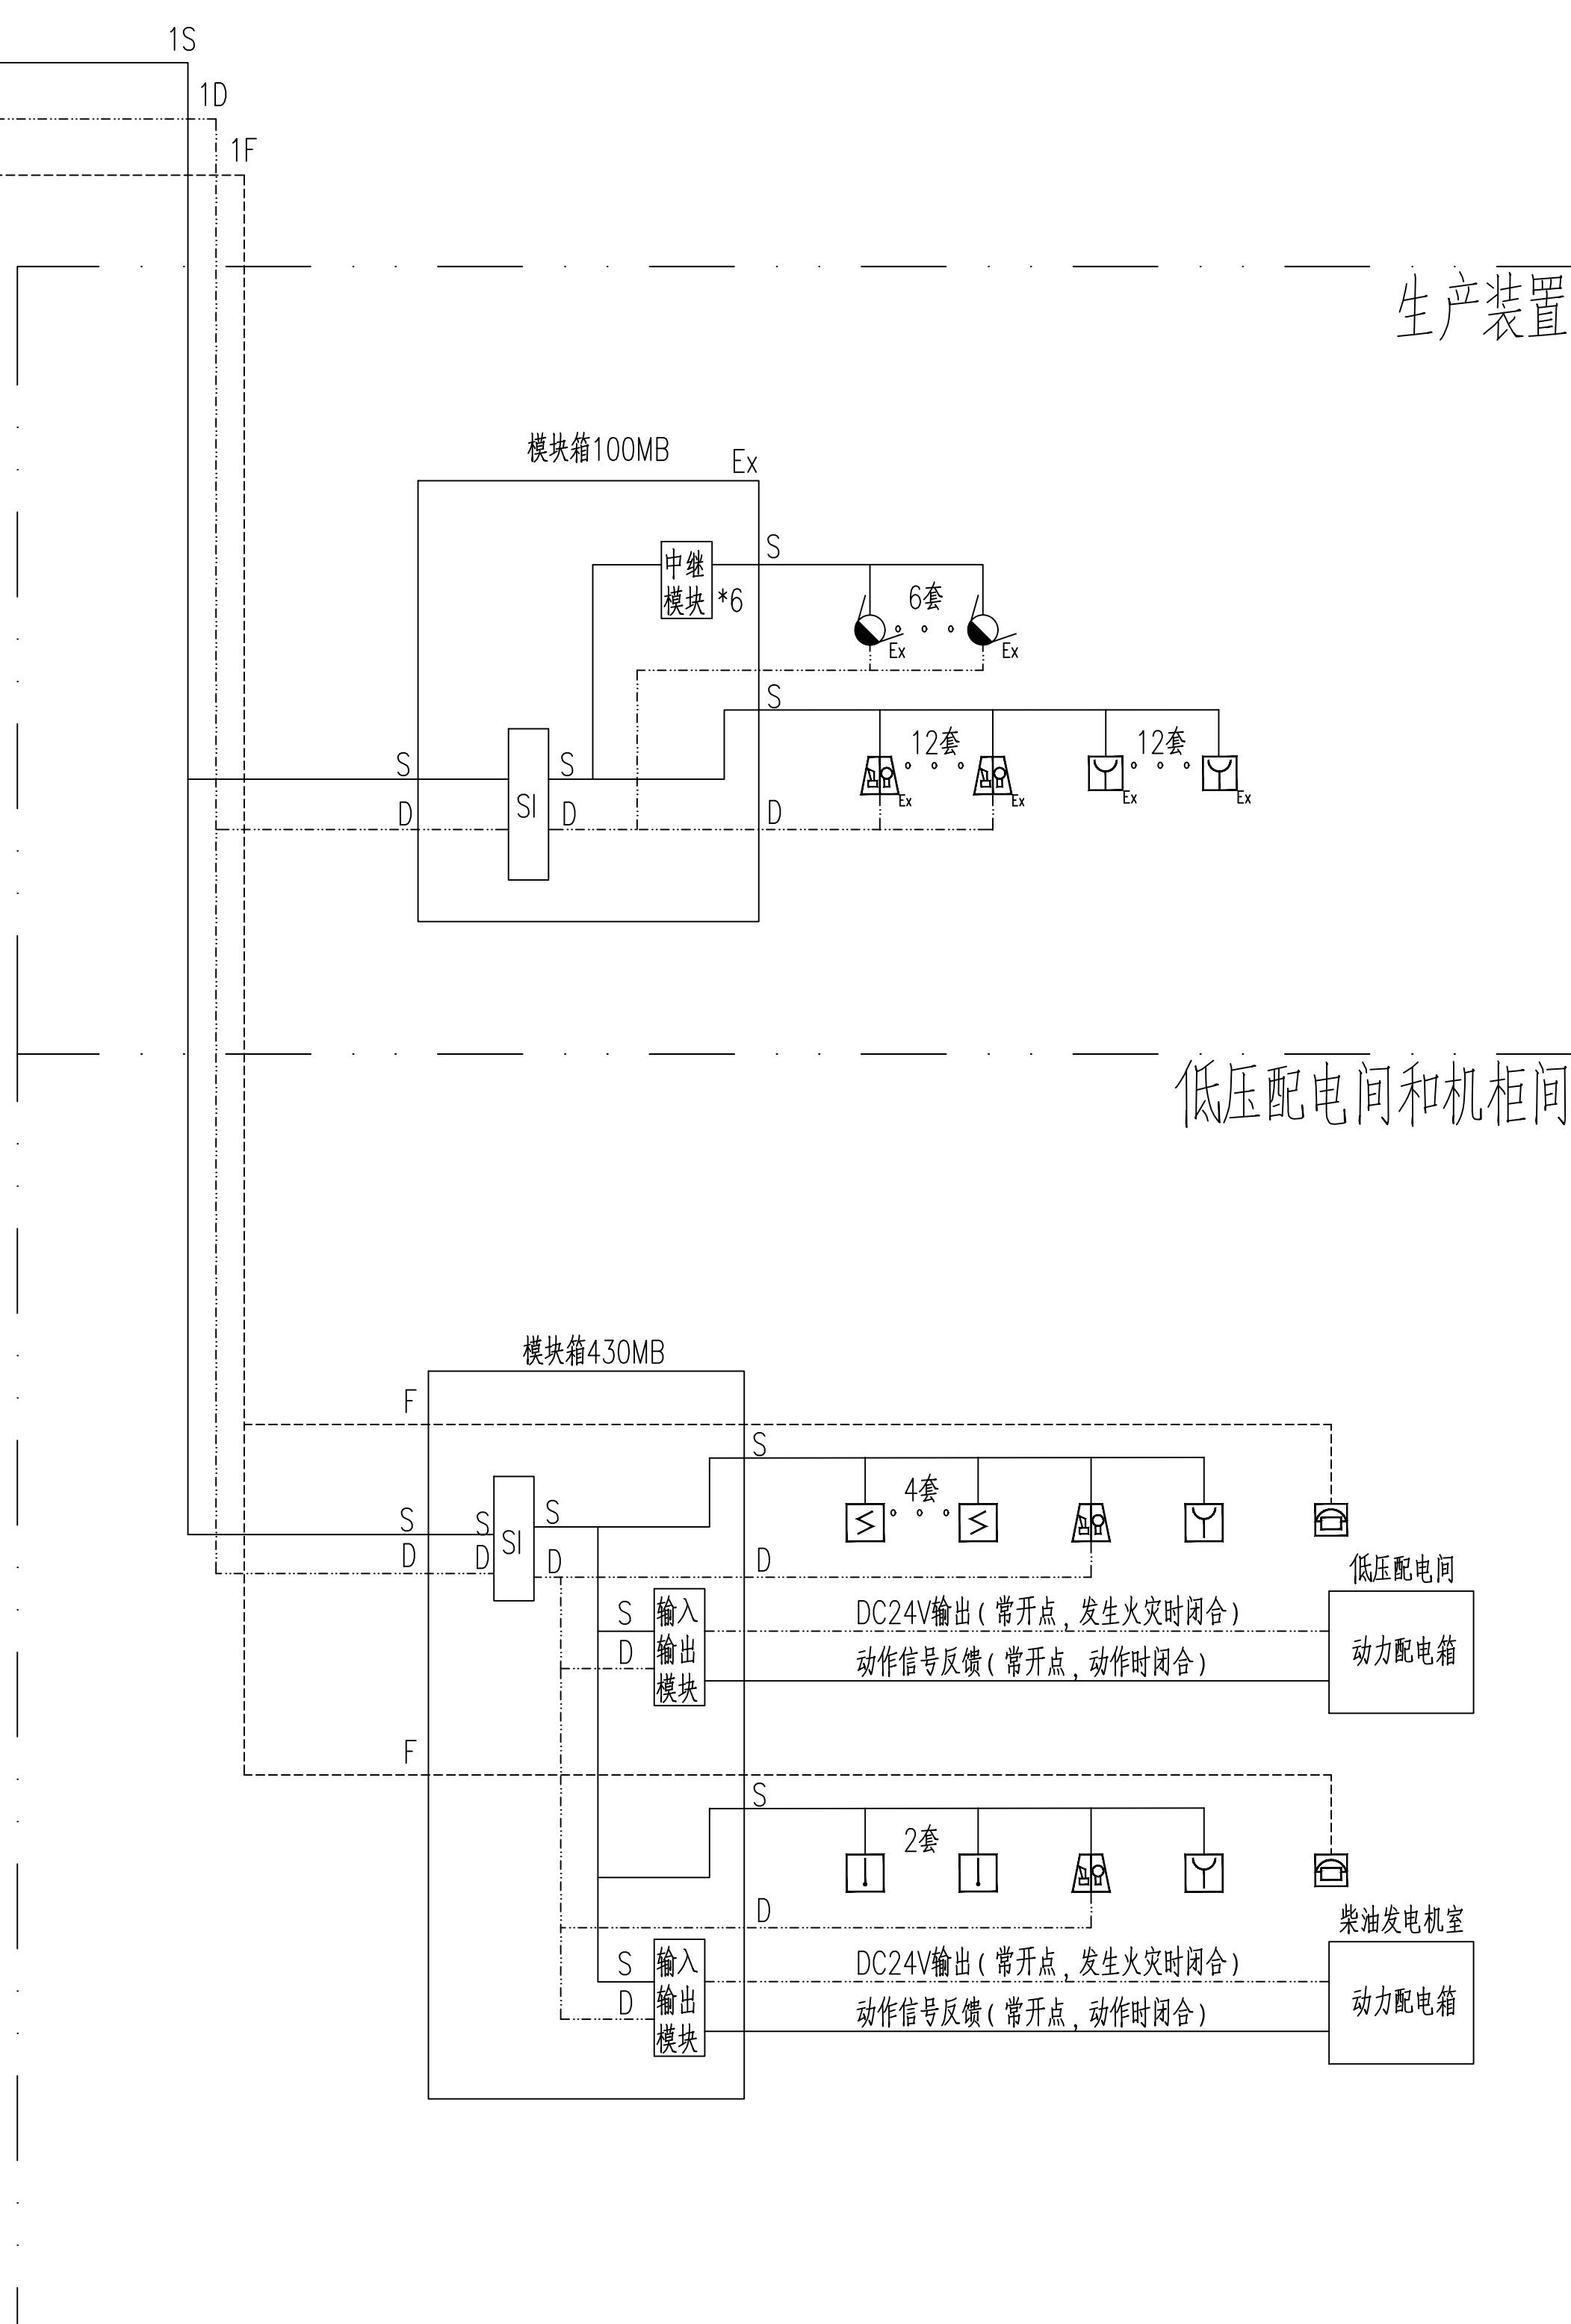


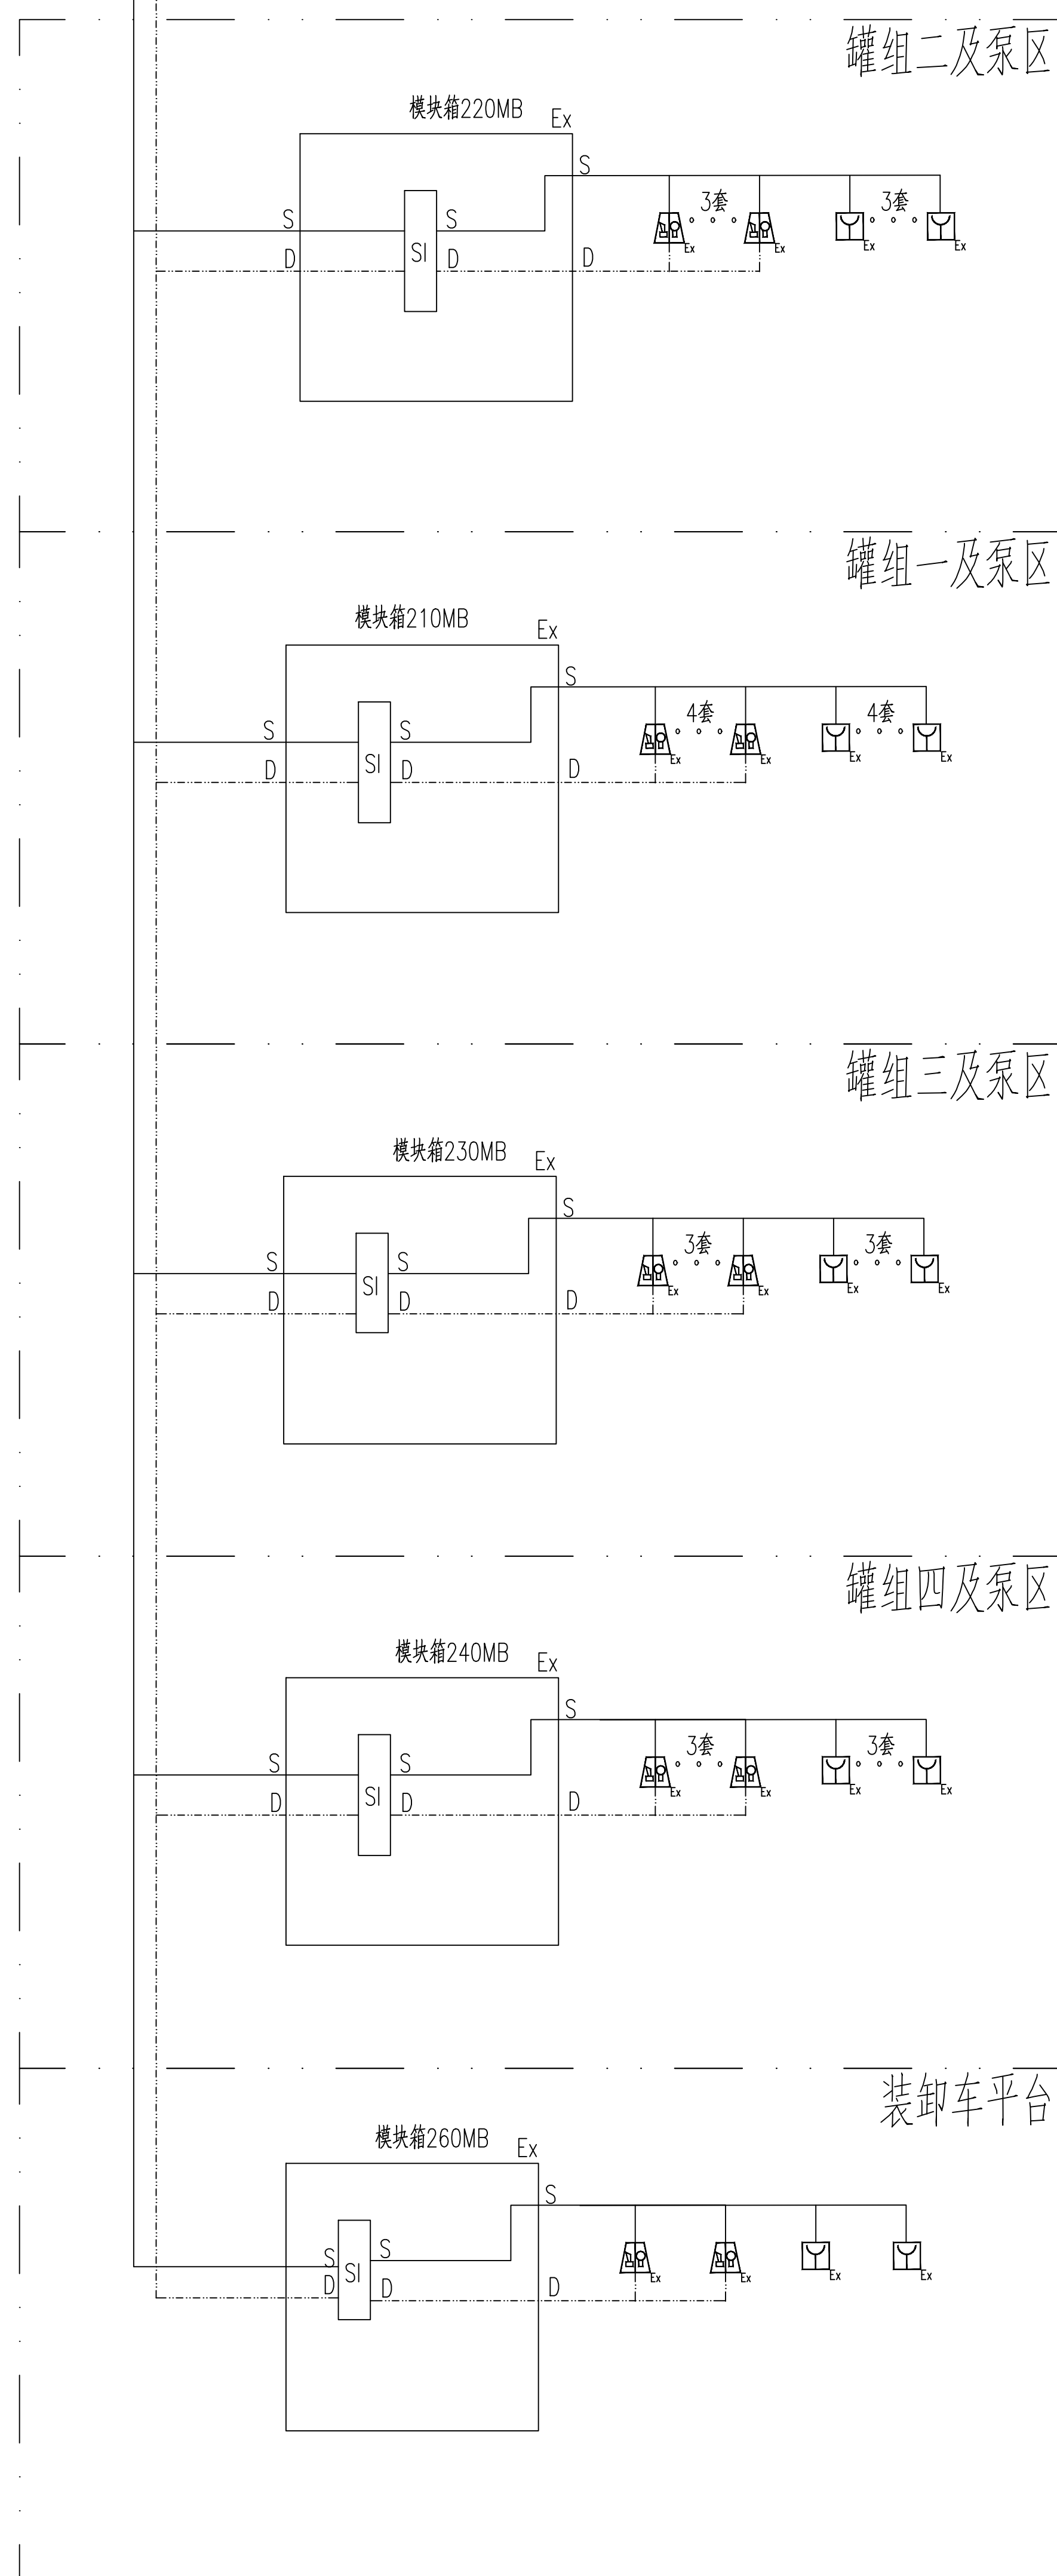

图例

| 符号                                                                                    | 设备名称      |
|---------------------------------------------------------------------------------------|-----------|
|  | 吸烟探测器     |
|  | 声光报警器     |
|  | 手动报警按钮    |
|  | 消防应急广播扬声器 |
|  | 消防电话      |
|  | 防爆型火焰探测器  |
|  | 防爆型声光报警器  |
|  | 防爆型手动火灾按钮 |
|  | 手动报警按钮    |
| S                                                                                     | 报警二总线     |
| D                                                                                     | 24V电源线    |
| F                                                                                     | 消防广播线路    |
| BC                                                                                    | 消防电话线路    |
| C                                                                                     | 消防电源监控线路  |

说明:本图根据“南京金陵石化工程设计有限公司,南京长江江宇环保科技有限公司 5万吨/年电子化学品精制再生循环利用项目 全厂电信 火灾报警系统 火灾报警系统图 22163AS060TC01DW01A0”进行绘制。
 
|   |                  |  |  |  |  |              |                   |      |        |            |
|---|------------------|--|--|--|--|--------------|-------------------|------|--------|------------|
|   |                  |  |  |  |  | 潘建斌          | 王如                | 吴圣华  |        | 2025.11.12 |
|   |                  |  |  |  |  | 自撰文          | 吴楚红               | 吴圣华  |        | 2025.11.12 |
| 版次   | 说 明              |  |  |  |  | 设计           | 校核                | 审核   | AUTH'D | 日期         |
| REV   | DESCRIPTION      |  |  |  |  | PRED         | CHKD              | APPR | DATE   |            |
|  <b>安徽华东化工医药工程有限责任公司</b><br>ANHUI HUADONG CHEMICAL AND MEDICAL ENGINEERING CO., LTD.<br>安徽省合肥市包河区包公祠街道包河花园二期B-2幢10楼<br>The copyright of this drawing is the property of ANHUI HUADONG CHEMICAL AND MEDICAL ENGINEERING CO., LTD.<br>Unauthorized reproduction or duplication to the third party is not permitted. |                  |  |  |  |  |              |                   |      |        |            |
| CUSTOMER   | 南京长江生态环保科技股份有限公司 |  |  |  |  | 图名           | 全厂污水处理站工艺总图（二）    |      |        |            |
| PROJECT   | 综合利用能力化提升项目      |  |  |  |  | DRAWING NAME |                   |      |        |            |
| DESIGN AREA   | 专业设计             |  |  |  |  | 项目编号         | N25022            |      |        |            |
| REVISION AREA   | 修改内容             |  |  |  |  | 图号           | DRAWING NO.       |      |        |            |
| 施工区   | 电话               |  |  |  |  | 比例           | /                 |      |        |            |
|   |                  |  |  |  |  | 图号           | N25022D02C10D1W02 |      |        |            |

工程勘察资质(出图)专用章  
安徽华东化工医药工程有限责任公司  
化工石化医药行业甲级 证书编号: A134008172  
中华人民共和国住房和城乡建设部监制  
有效期至2029年09月20日